

TUTORIAL TÉCNICO

Principais esquemas de ligação
no controlador de acesso
Digiprox SA 202



- ○ ○ ○
- ○ ○ ○
- ○ ○ ○
- ○ ○ ○

TUTORIAL TÉCNICO

Principais esquemas de ligação no controlador de acesso Digiprox SA 202

DIGIPROX SA 202



Suporte a clientes: [intelbras.com/pt-br/contato/suporte-tecnico/](https://www.intelbras.com/pt-br/contato/suporte-tecnico/)

Vídeo tutorial: [youtube.com/IntelbrasBR](https://www.youtube.com/IntelbrasBR)

(48) 2106 0006 | Segunda a sexta: 8h às 20h | Sábado: 8h às 18h

TUTORIAL TÉCNICO

Principais esquemas de ligação no controlador de acesso Digiprox SA 202

Neste tutorial você irá aprender **como realizar alguns esquemas de ligação no controlador de acesso Digiprox SA 202.**

01 FONTE DE ALIMENTAÇÃO

02 FECHADURA-ELETROIMÃ

03 FECHADURA ELETROMECHANICA

04 FECHADURA SOLENOIDE

05 FECHADURA SOLENOIDE (2 FIOS)

06 BOTÃO DE SAÍDA

07 CAMPAINHA



Suporte a clientes: intelbras.com/pt-br/contato/suporte-tecnico/

Vídeo tutorial: youtube.com/IntelbrasBR


(48) 2106 0006 | Segunda a sexta: 8h às 20h | Sábado: 8h às 18h

TUTORIAL TÉCNICO

Principais esquemas de ligação no
controlador de acesso Digiprox SA 202


01

FONTE DE ALIMENTAÇÃO

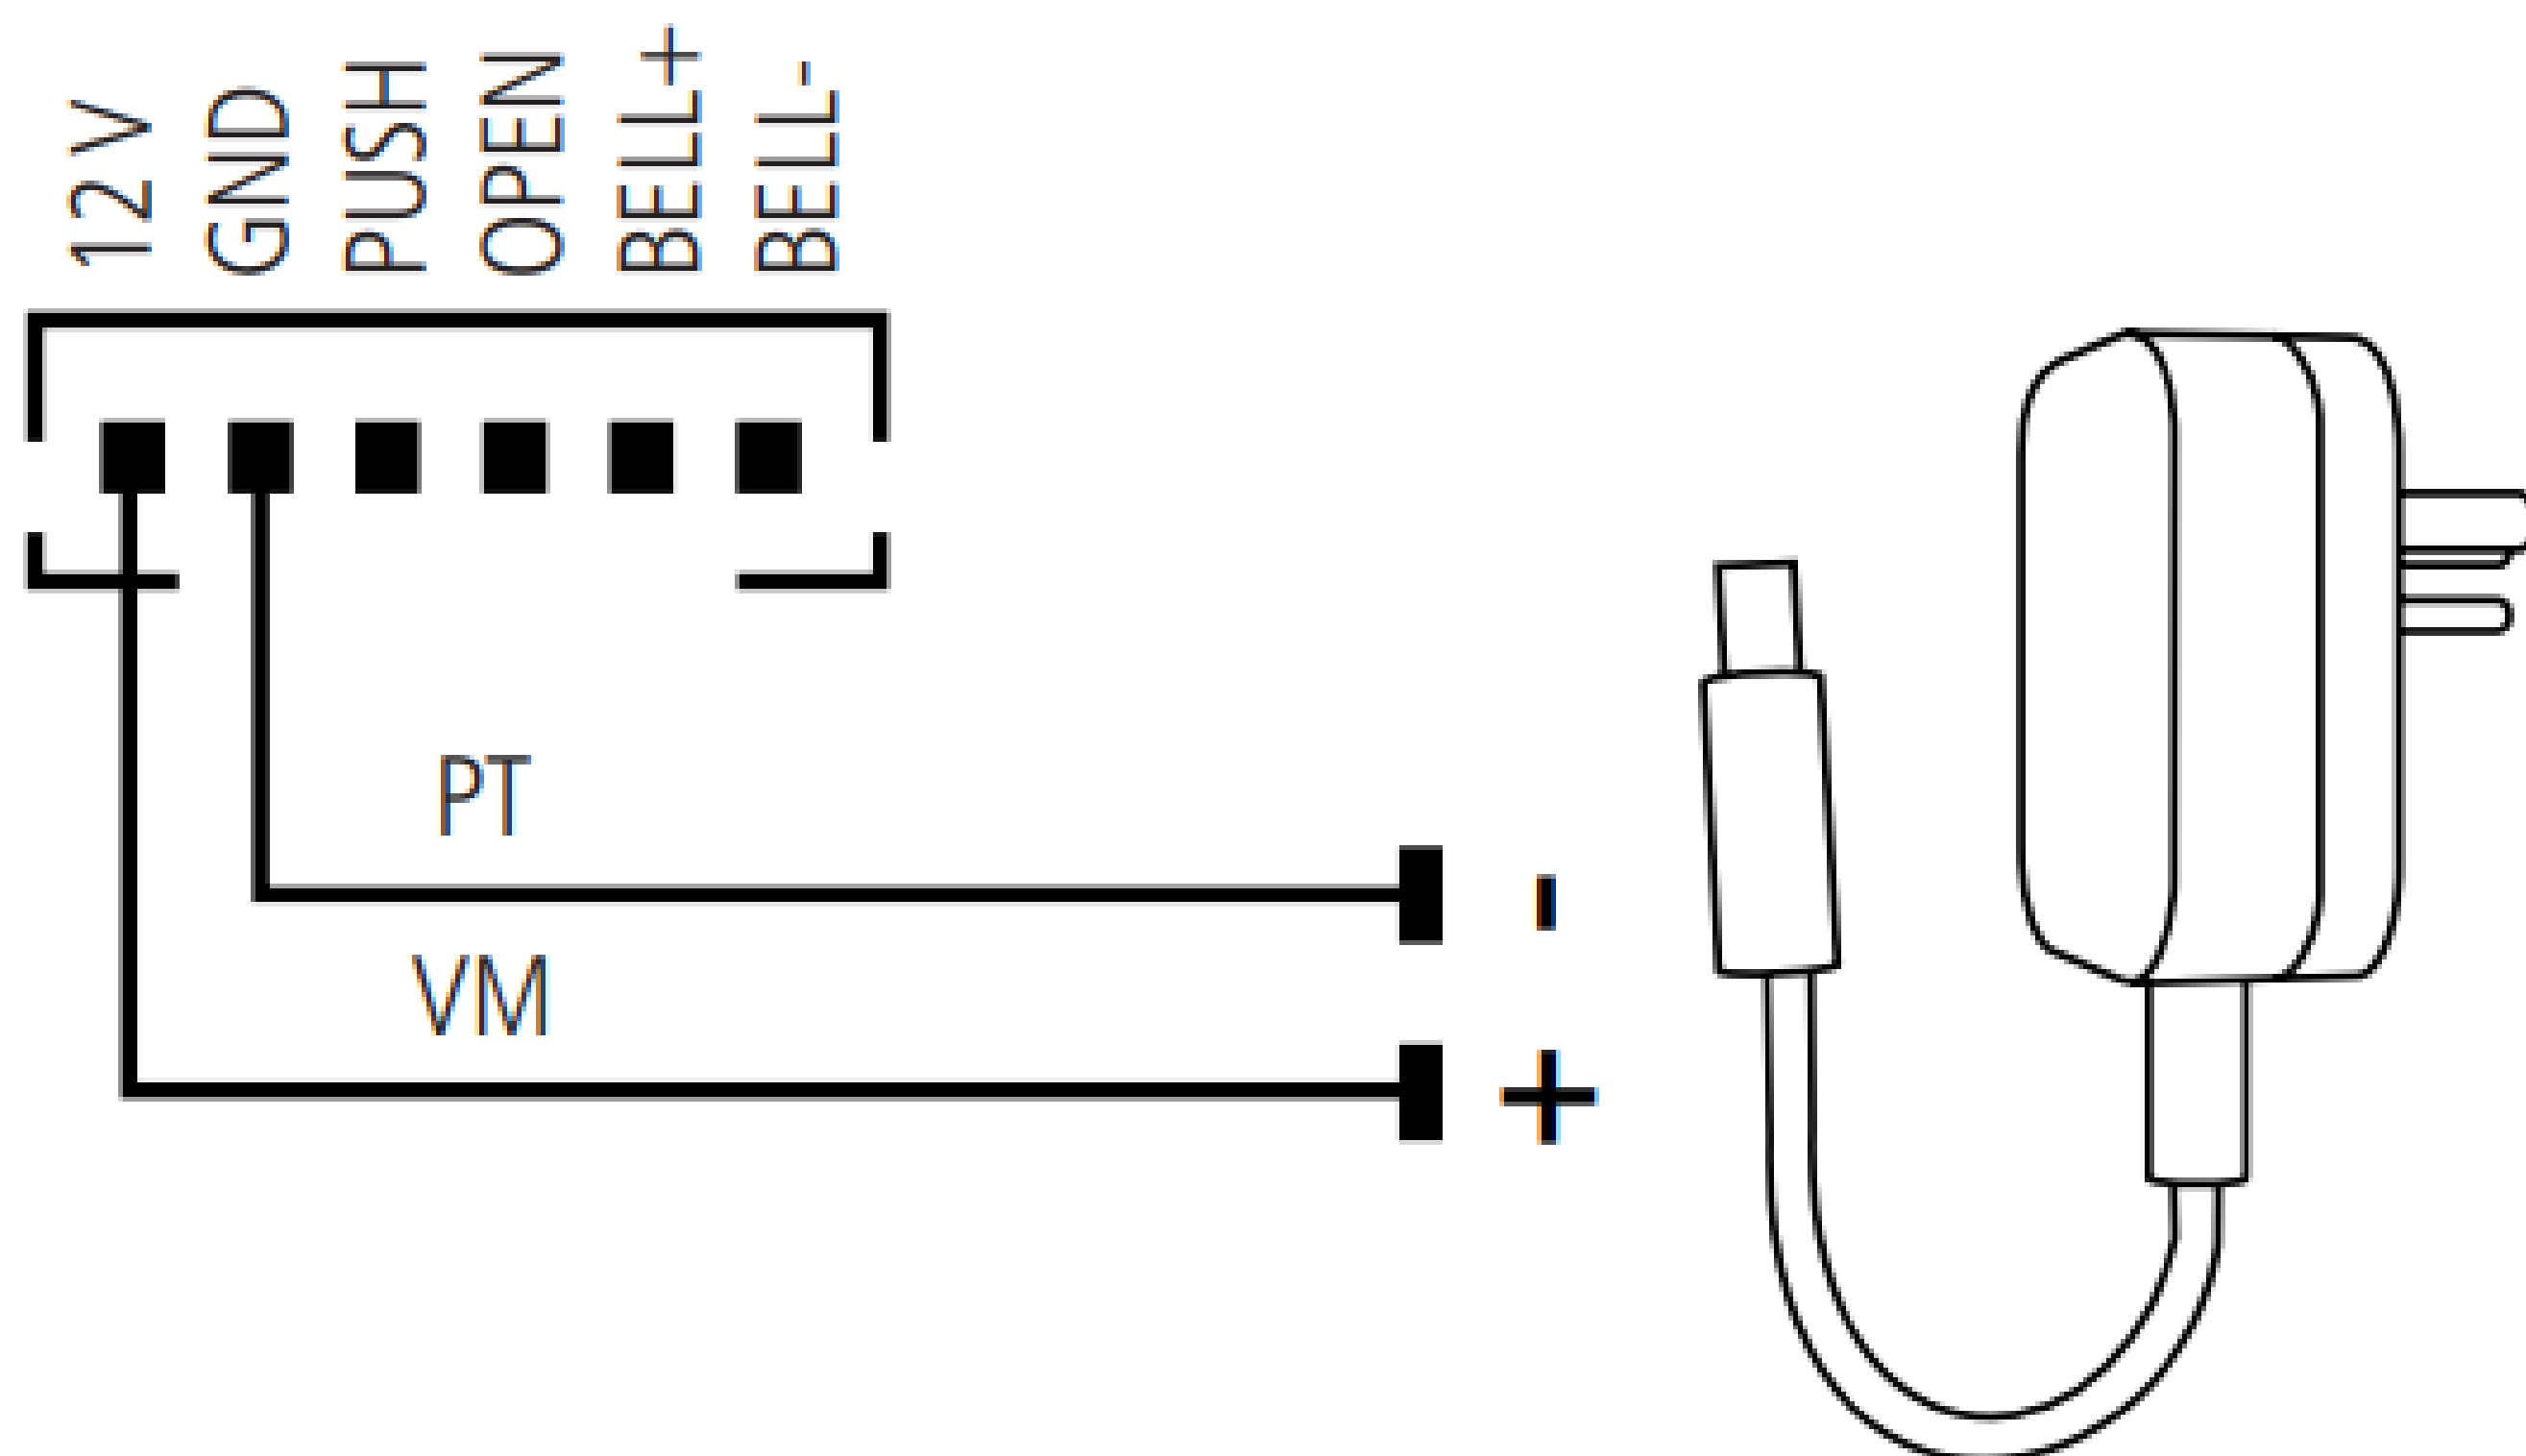

Fonte de alimentação

Caso **não haja nobreak** para alimentar o equipamento em situações de **queda de energia**, é recomendável a **instalação** de uma **fonte de alimentação** que possua **bateria**.

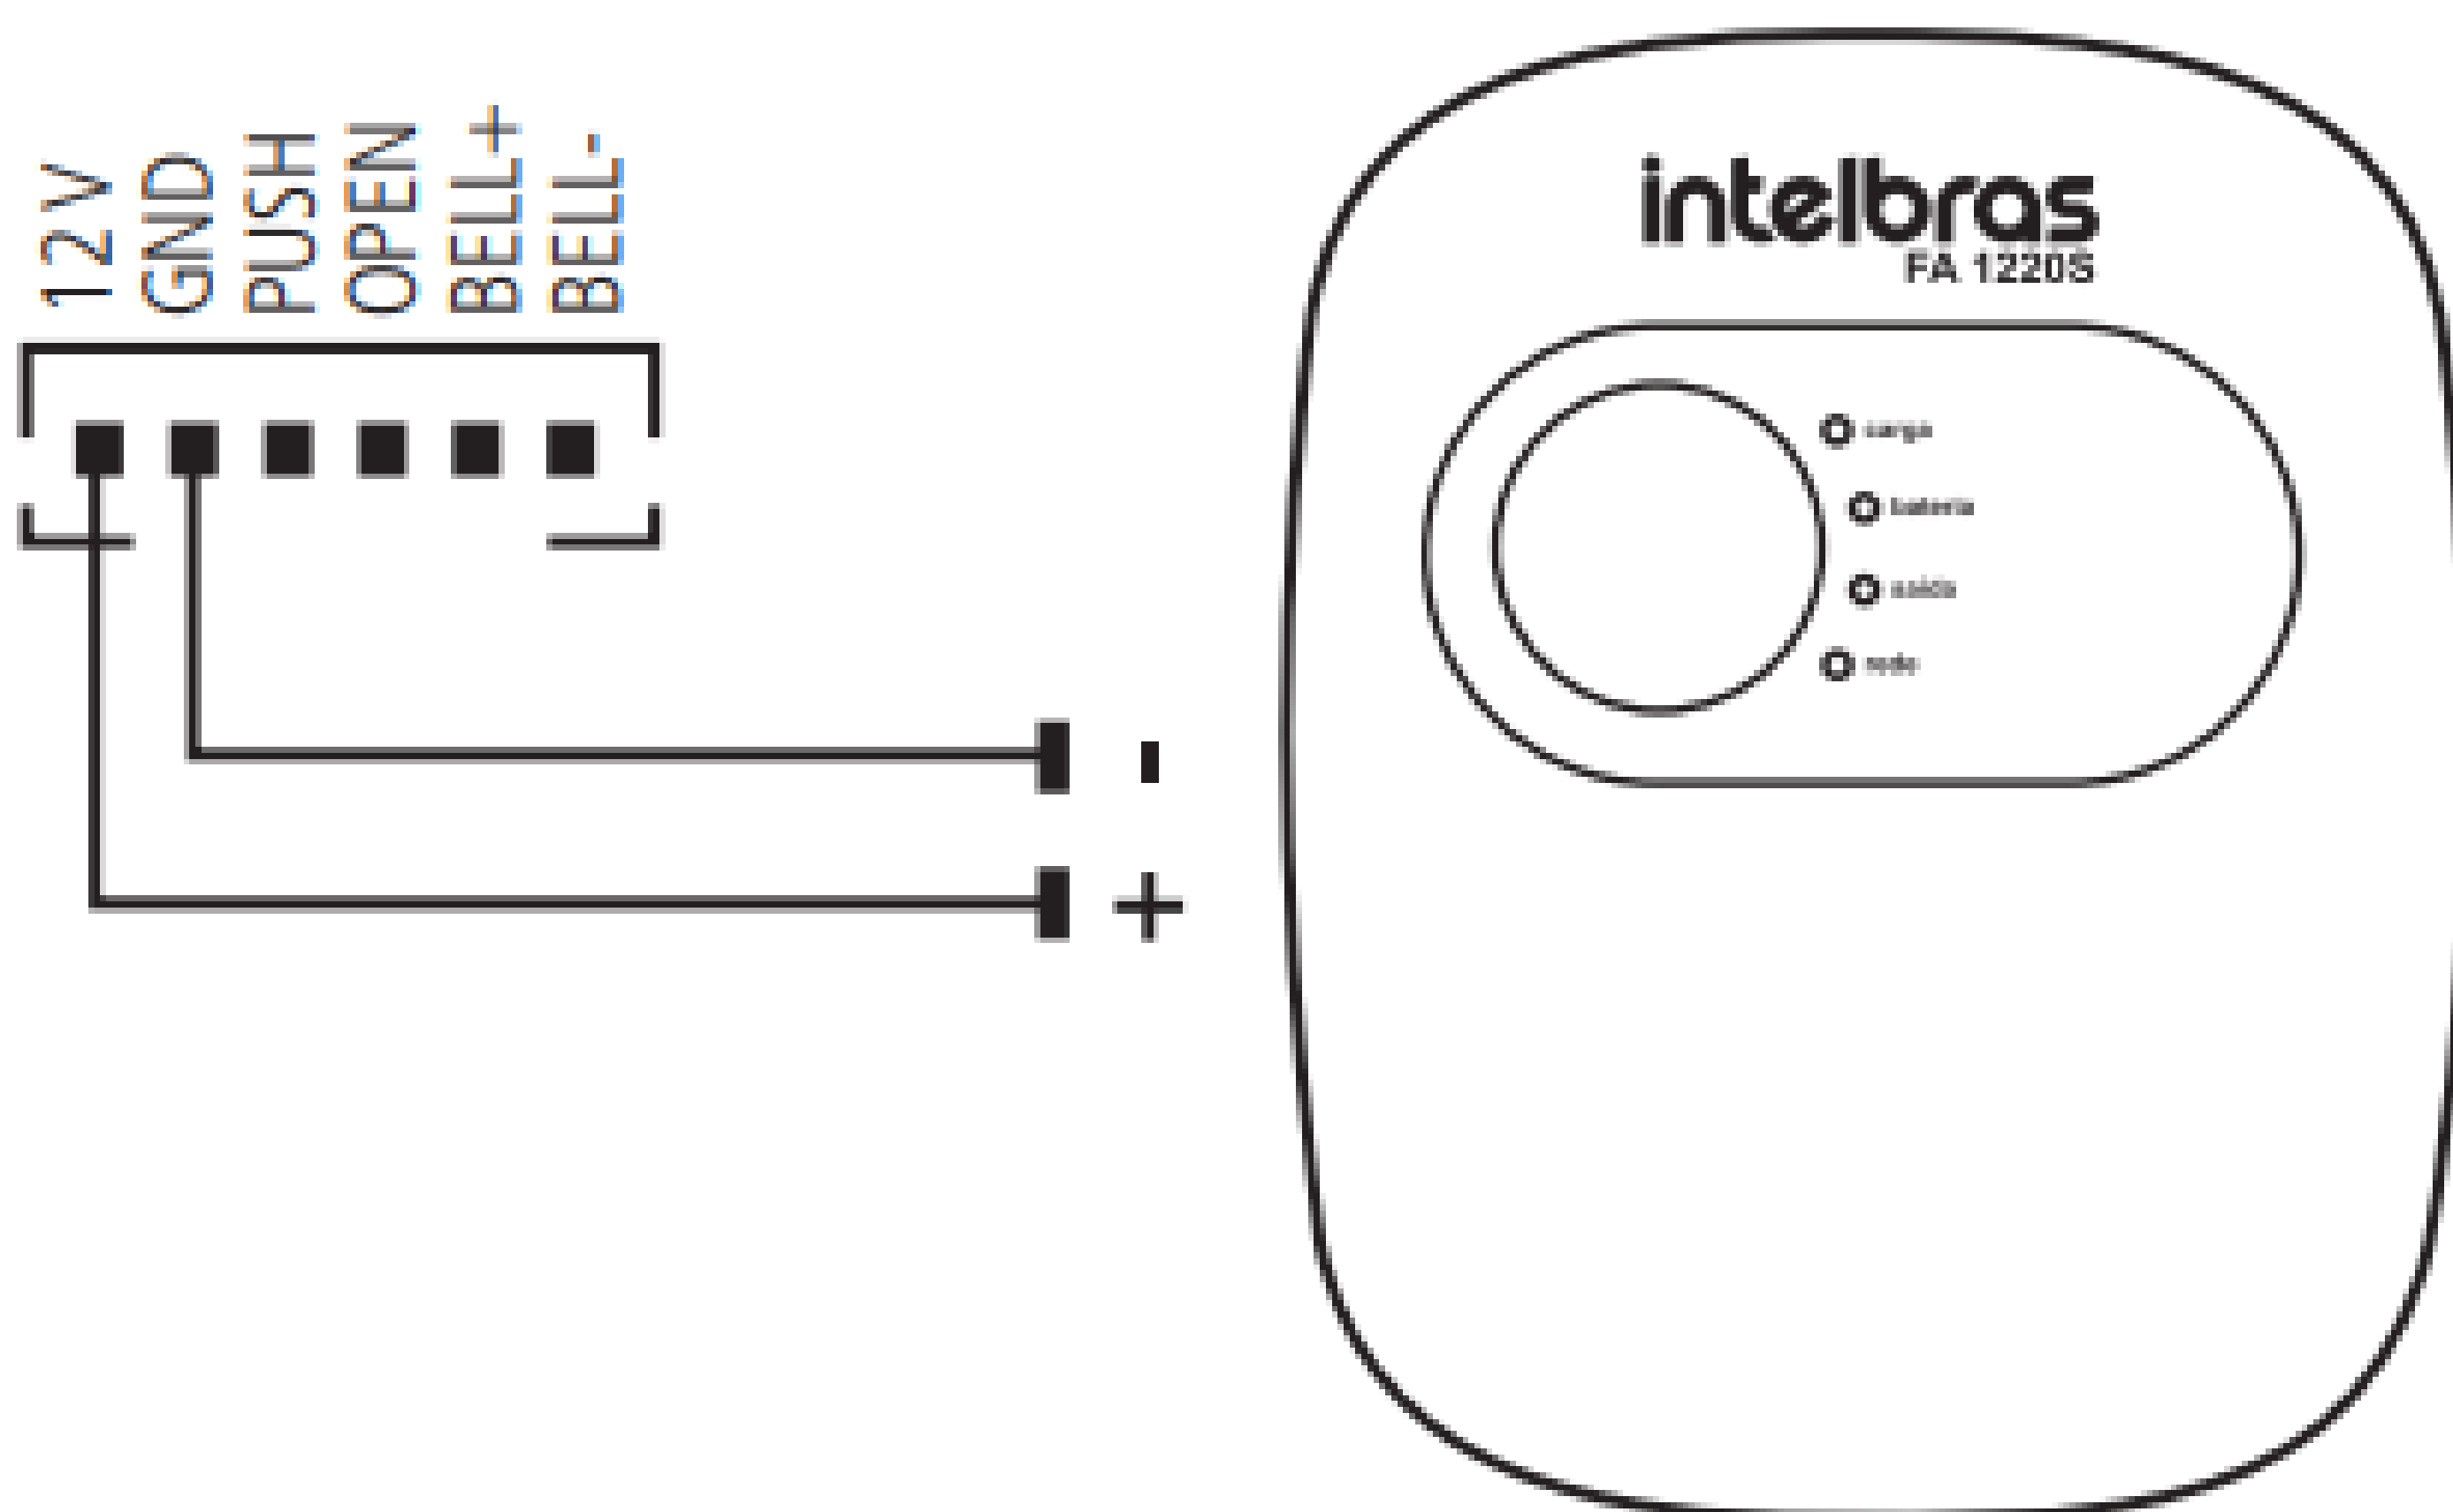

Fonte de alimentação com bateria

Suporte a clientes: intelbras.com/pt-br/contato/suporte-tecnico/

Vídeo tutorial: youtube.com/IntelbrasBR


(48) 2106 0006 | Segunda a sexta: 8h às 20h | Sábado: 8h às 18h

TUTORIAL TÉCNICO

Principais esquemas de ligação no controlador de acesso Digiprox SA 202

02

FECHADURA-ELETROIMÃ

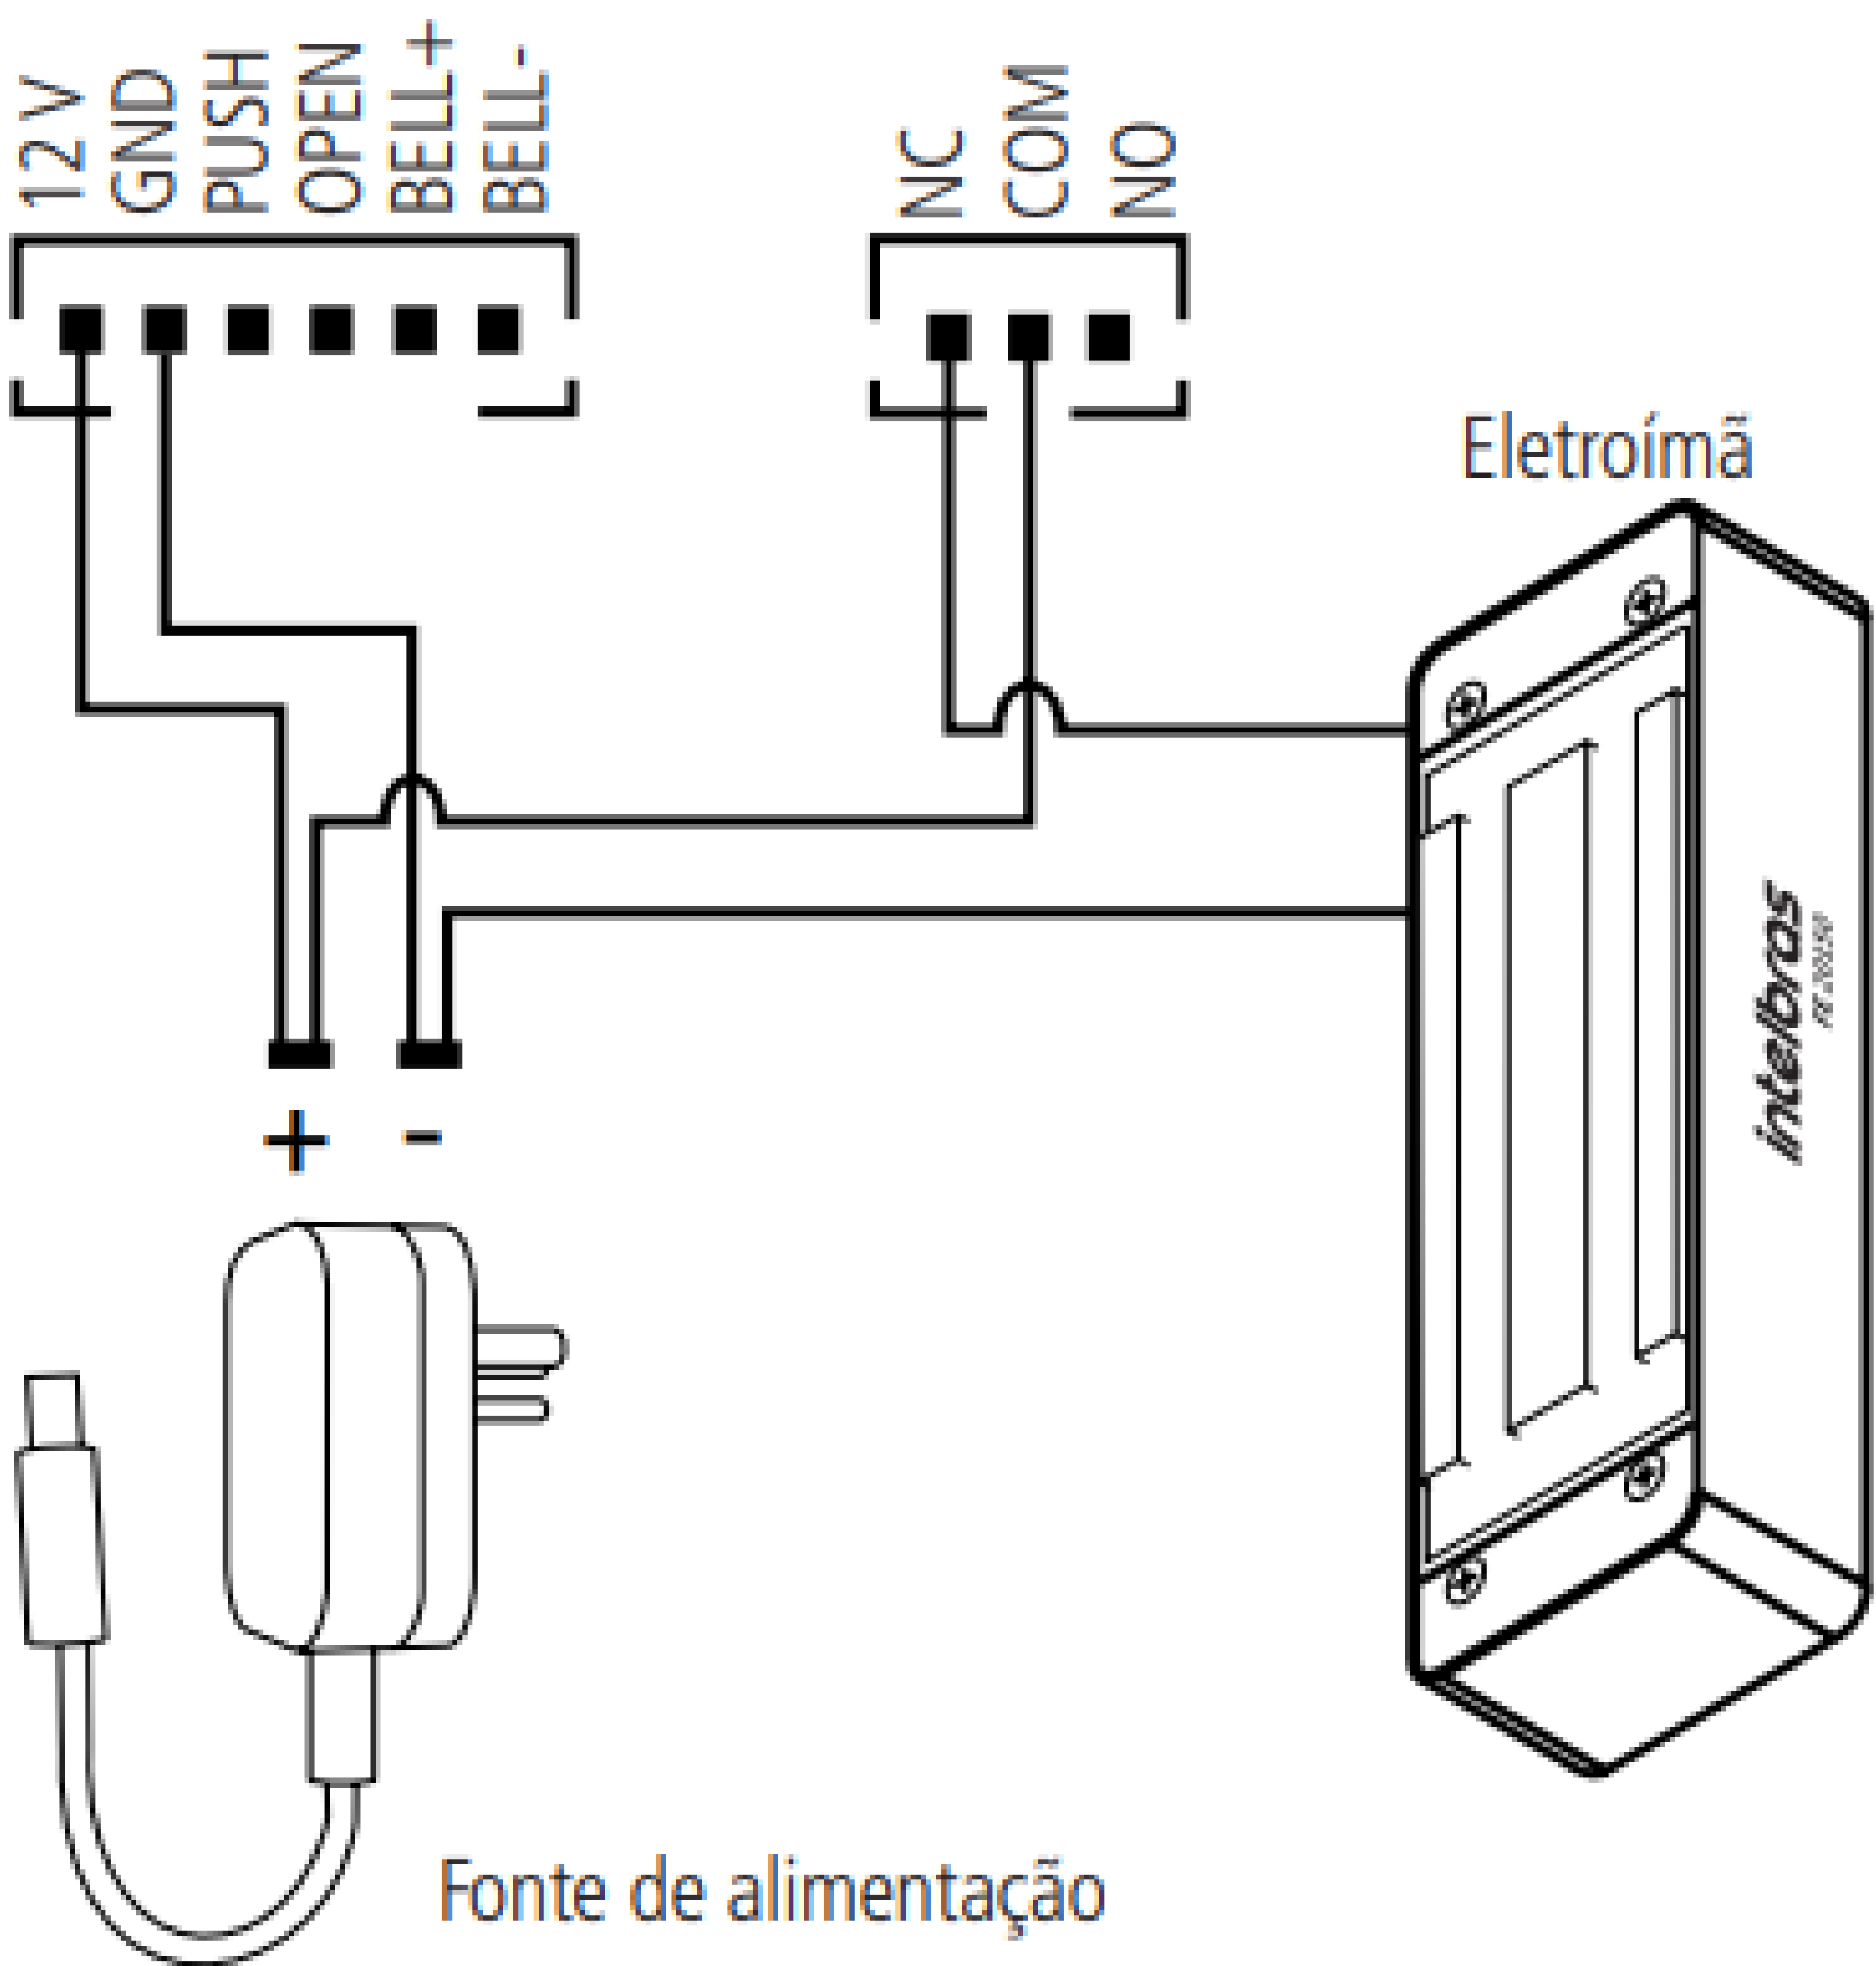

OBSERVAÇÃO

A corrente nominal de chaveamento para acionar as fechaduras nas saídas **NC**, **COM** e **NO** é de **1,5 A**.


Suporte a clientes: intelbras.com/pt-br/contato/suporte-tecnico/

Vídeo tutorial: youtube.com/IntelbrasBR

(48) 2106 0006 | Segunda a sexta: 8h às 20h | Sábado: 8h às 18h

03

FECHADURA ELETROMECHANICA

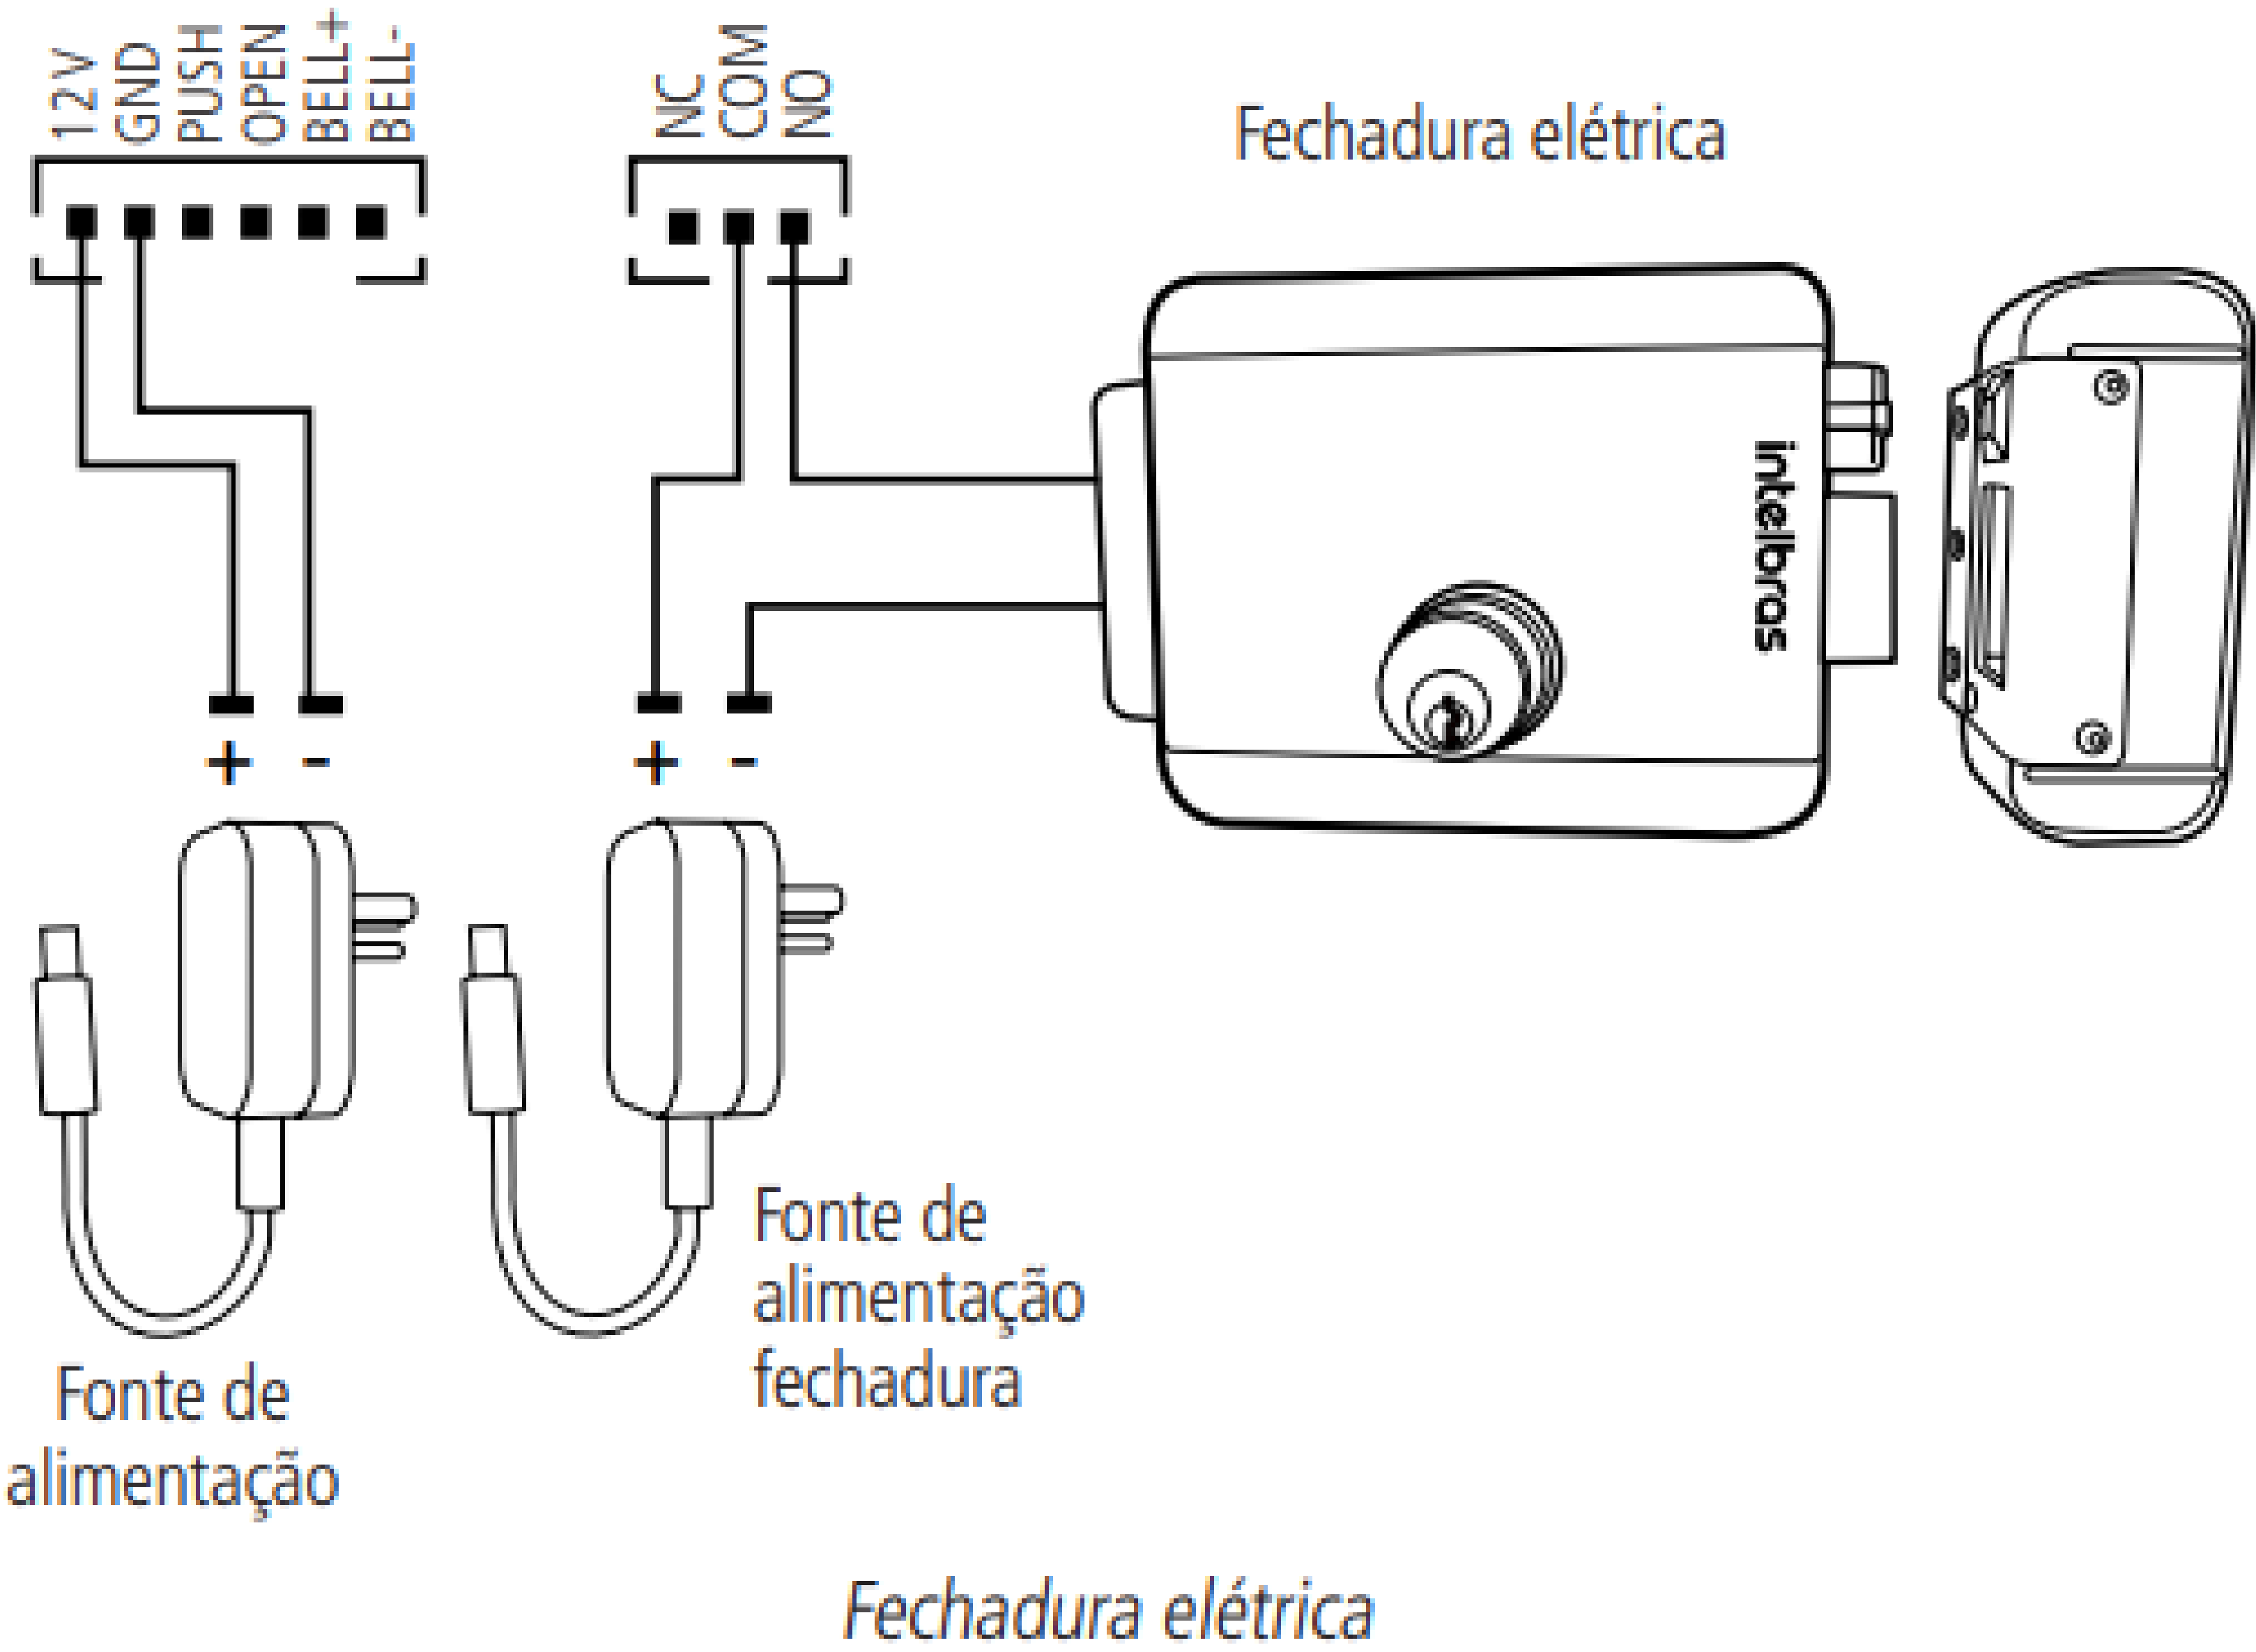


OBSERVAÇÃO

A corrente nominal de chaveamento para acionar as fechaduras nas saídas **NC**, **COM** e **NO** é de **1,5 A**.

04

FECHADURA SOLENOIDE

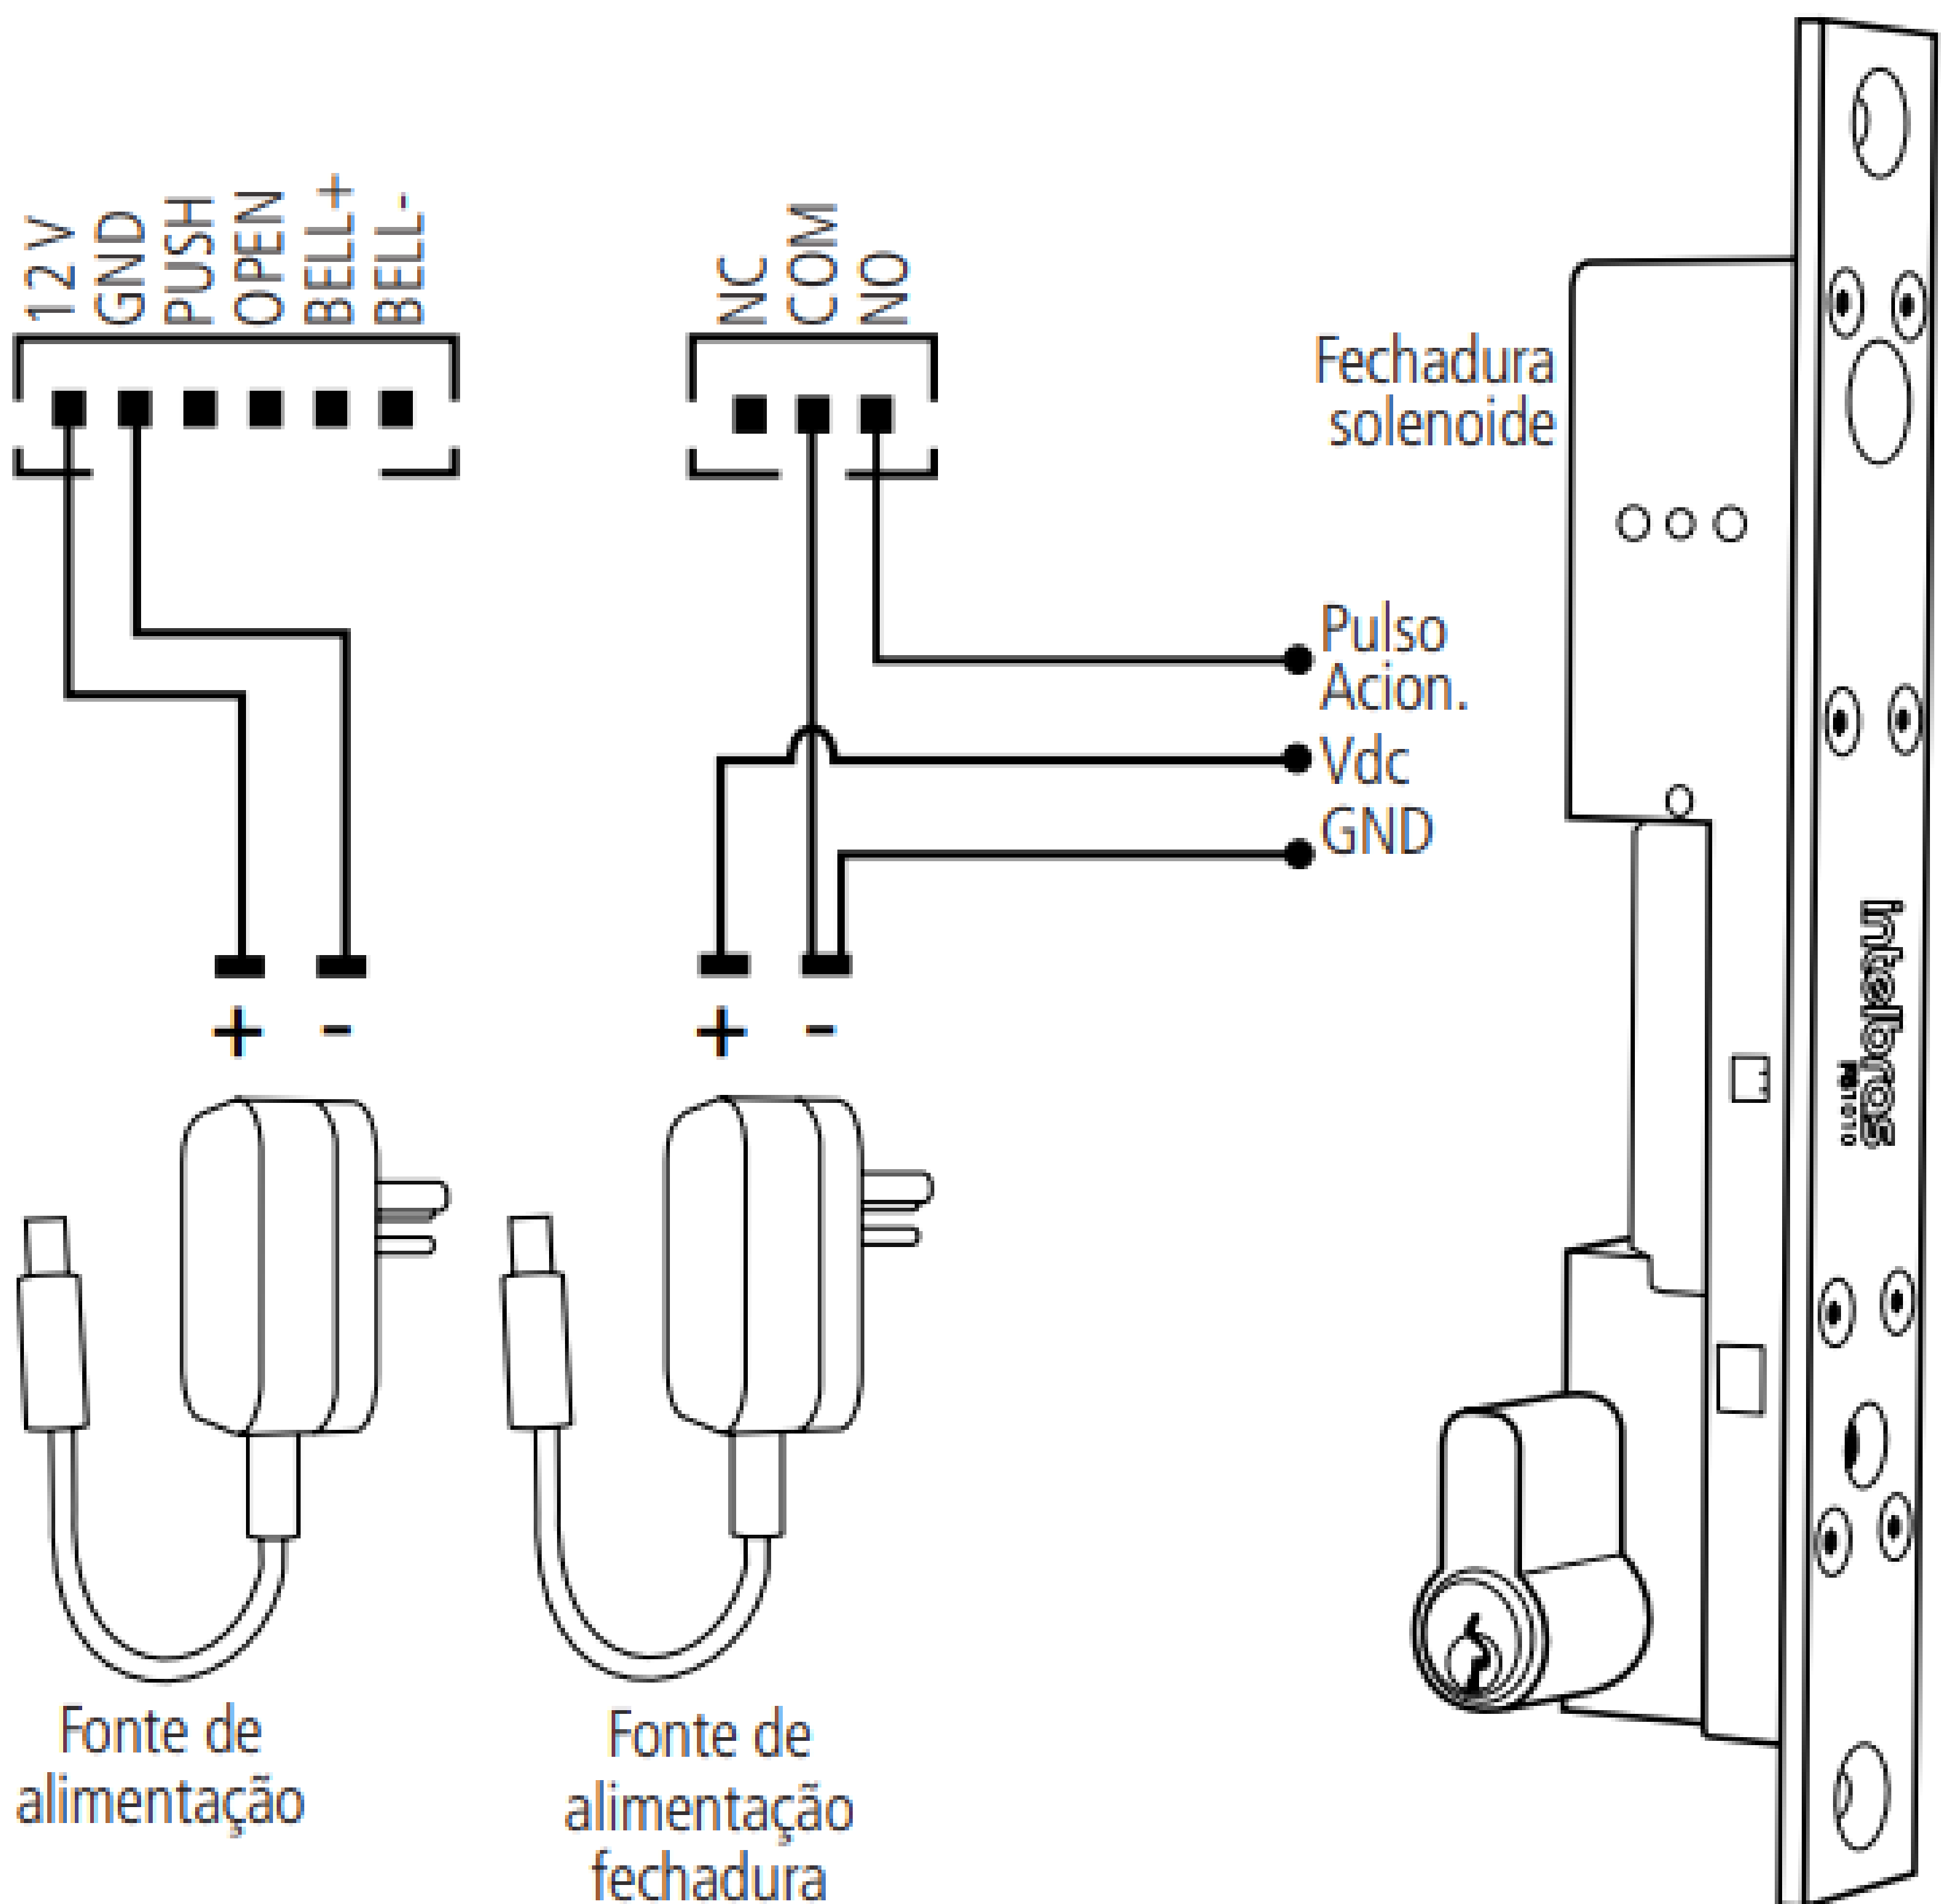

OBSERVAÇÃO


A corrente nominal de chaveamento para acionar as fechaduras nas saídas **NC**, **COM** e **NO** é de **1,5 A**.

TUTORIAL TÉCNICO

Principais esquemas de ligação no controlador de acesso Digiprox SA 202

05

FECHADURA SOLENOIDE (2 FIOS)

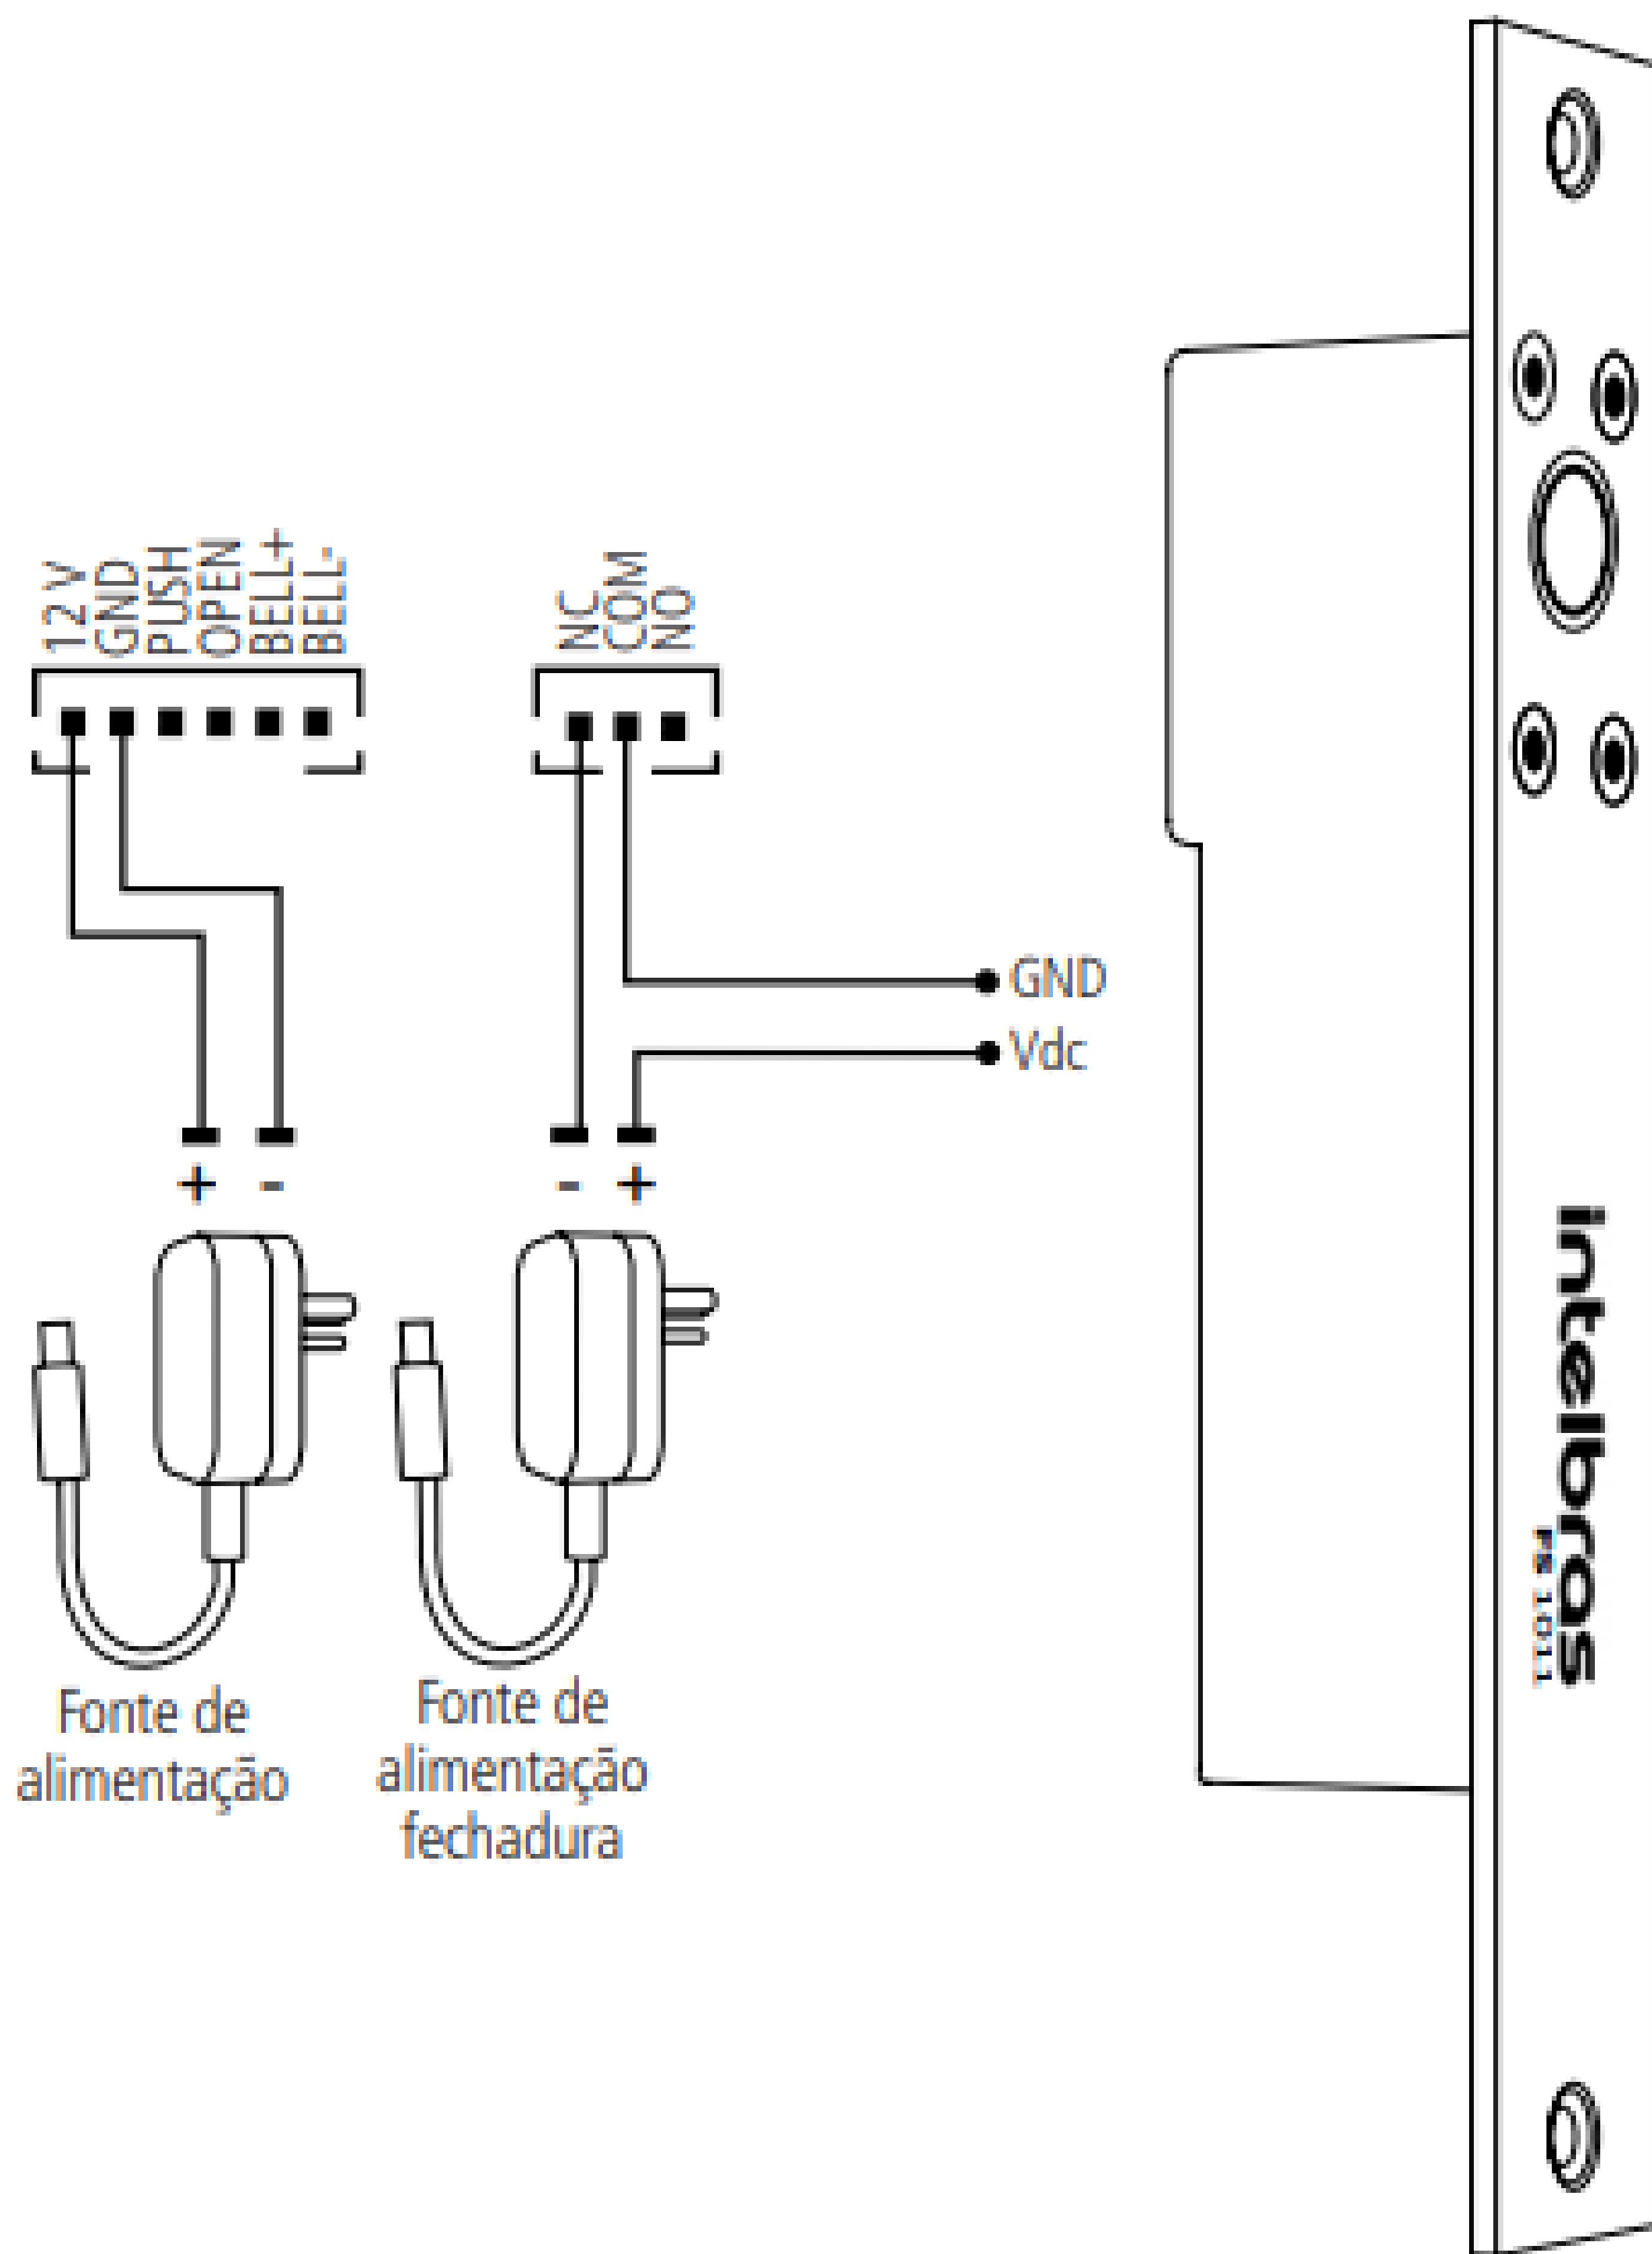

Suporte a clientes: intelbras.com/pt-br/contato/suporte-tecnico/


Vídeo tutorial: youtube.com/IntelbrasBR

(48) 2106 0006 | Segunda a sexta: 8h às 20h | Sábado: 8h às 18h

TUTORIAL TÉCNICO

Principais esquemas de ligação no controlador de acesso Digiprox SA 202

Para dispositivos similares de outro fabricante, utilizar um capacitor de **330 uF/25 V** em paralelo a alimentação da fechadura atentando para a polaridade do capacitor terminal menor, ou o marcado pela faixa branca, conectar ao **GND** e o outro no **Vdc**.

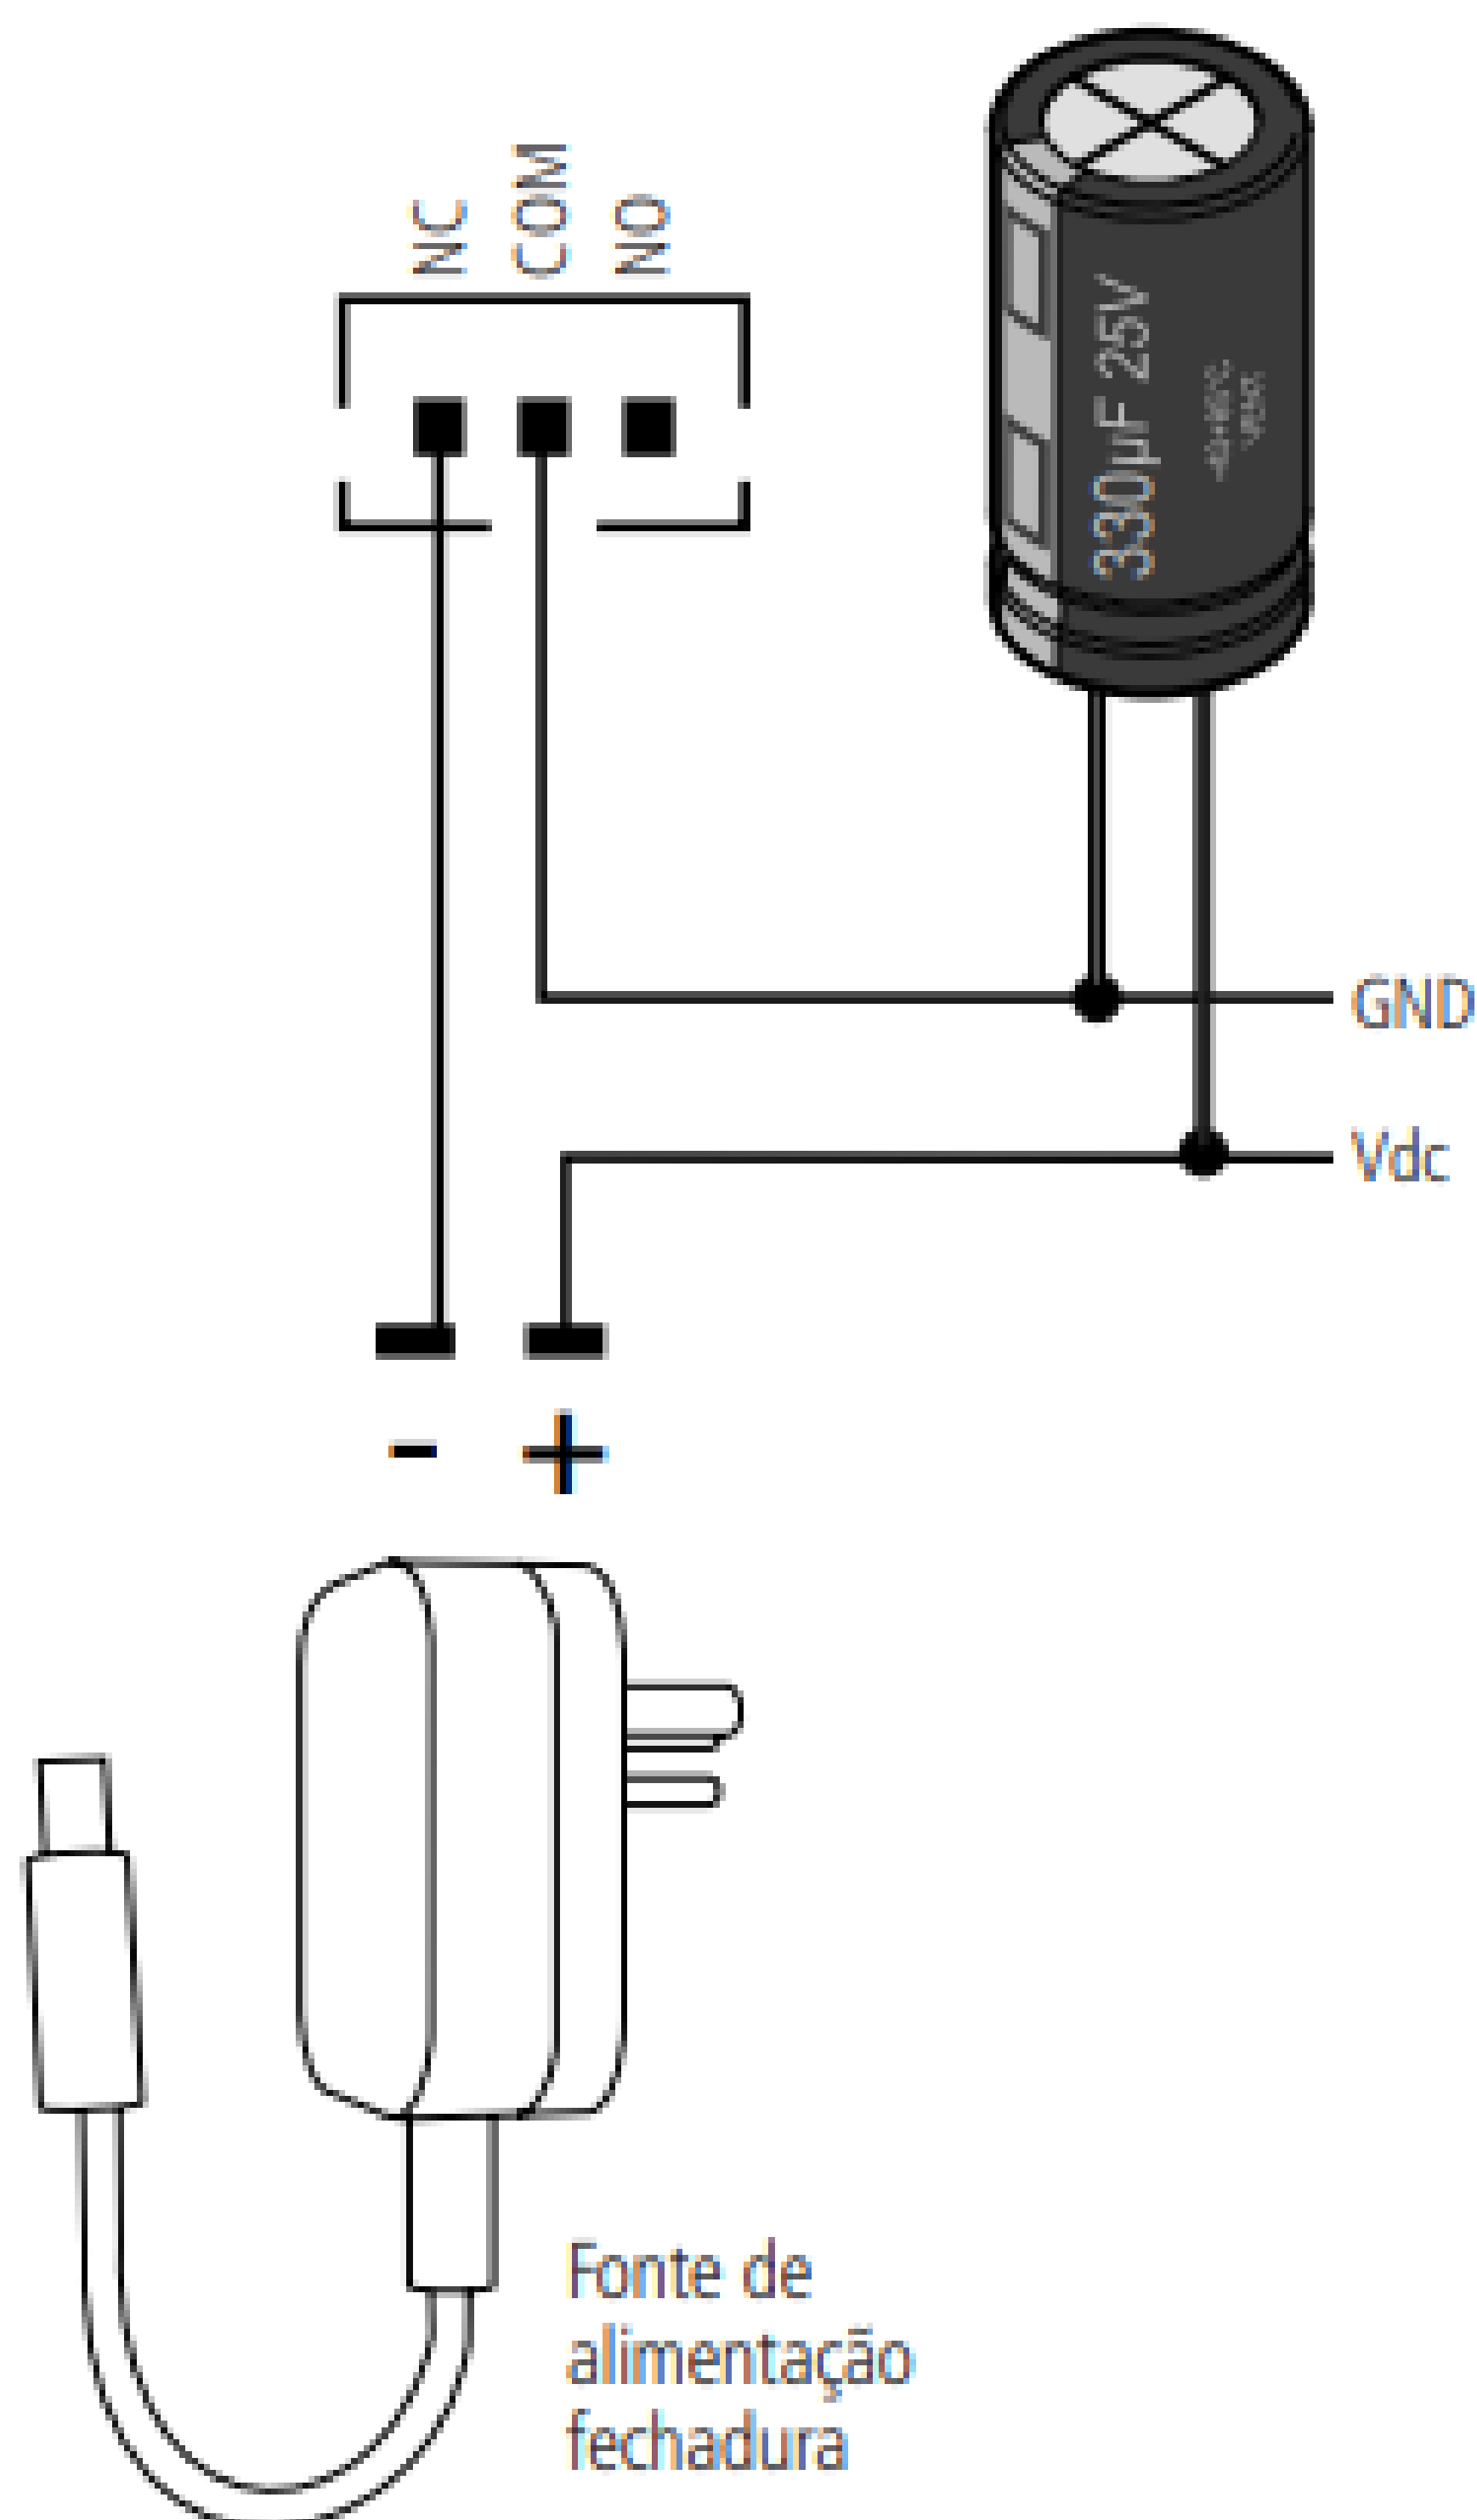


TUTORIAL TÉCNICO

Principais esquemas de ligação no controlador de acesso Digiprox SA 202

06

BOTÃO DE SAÍDA

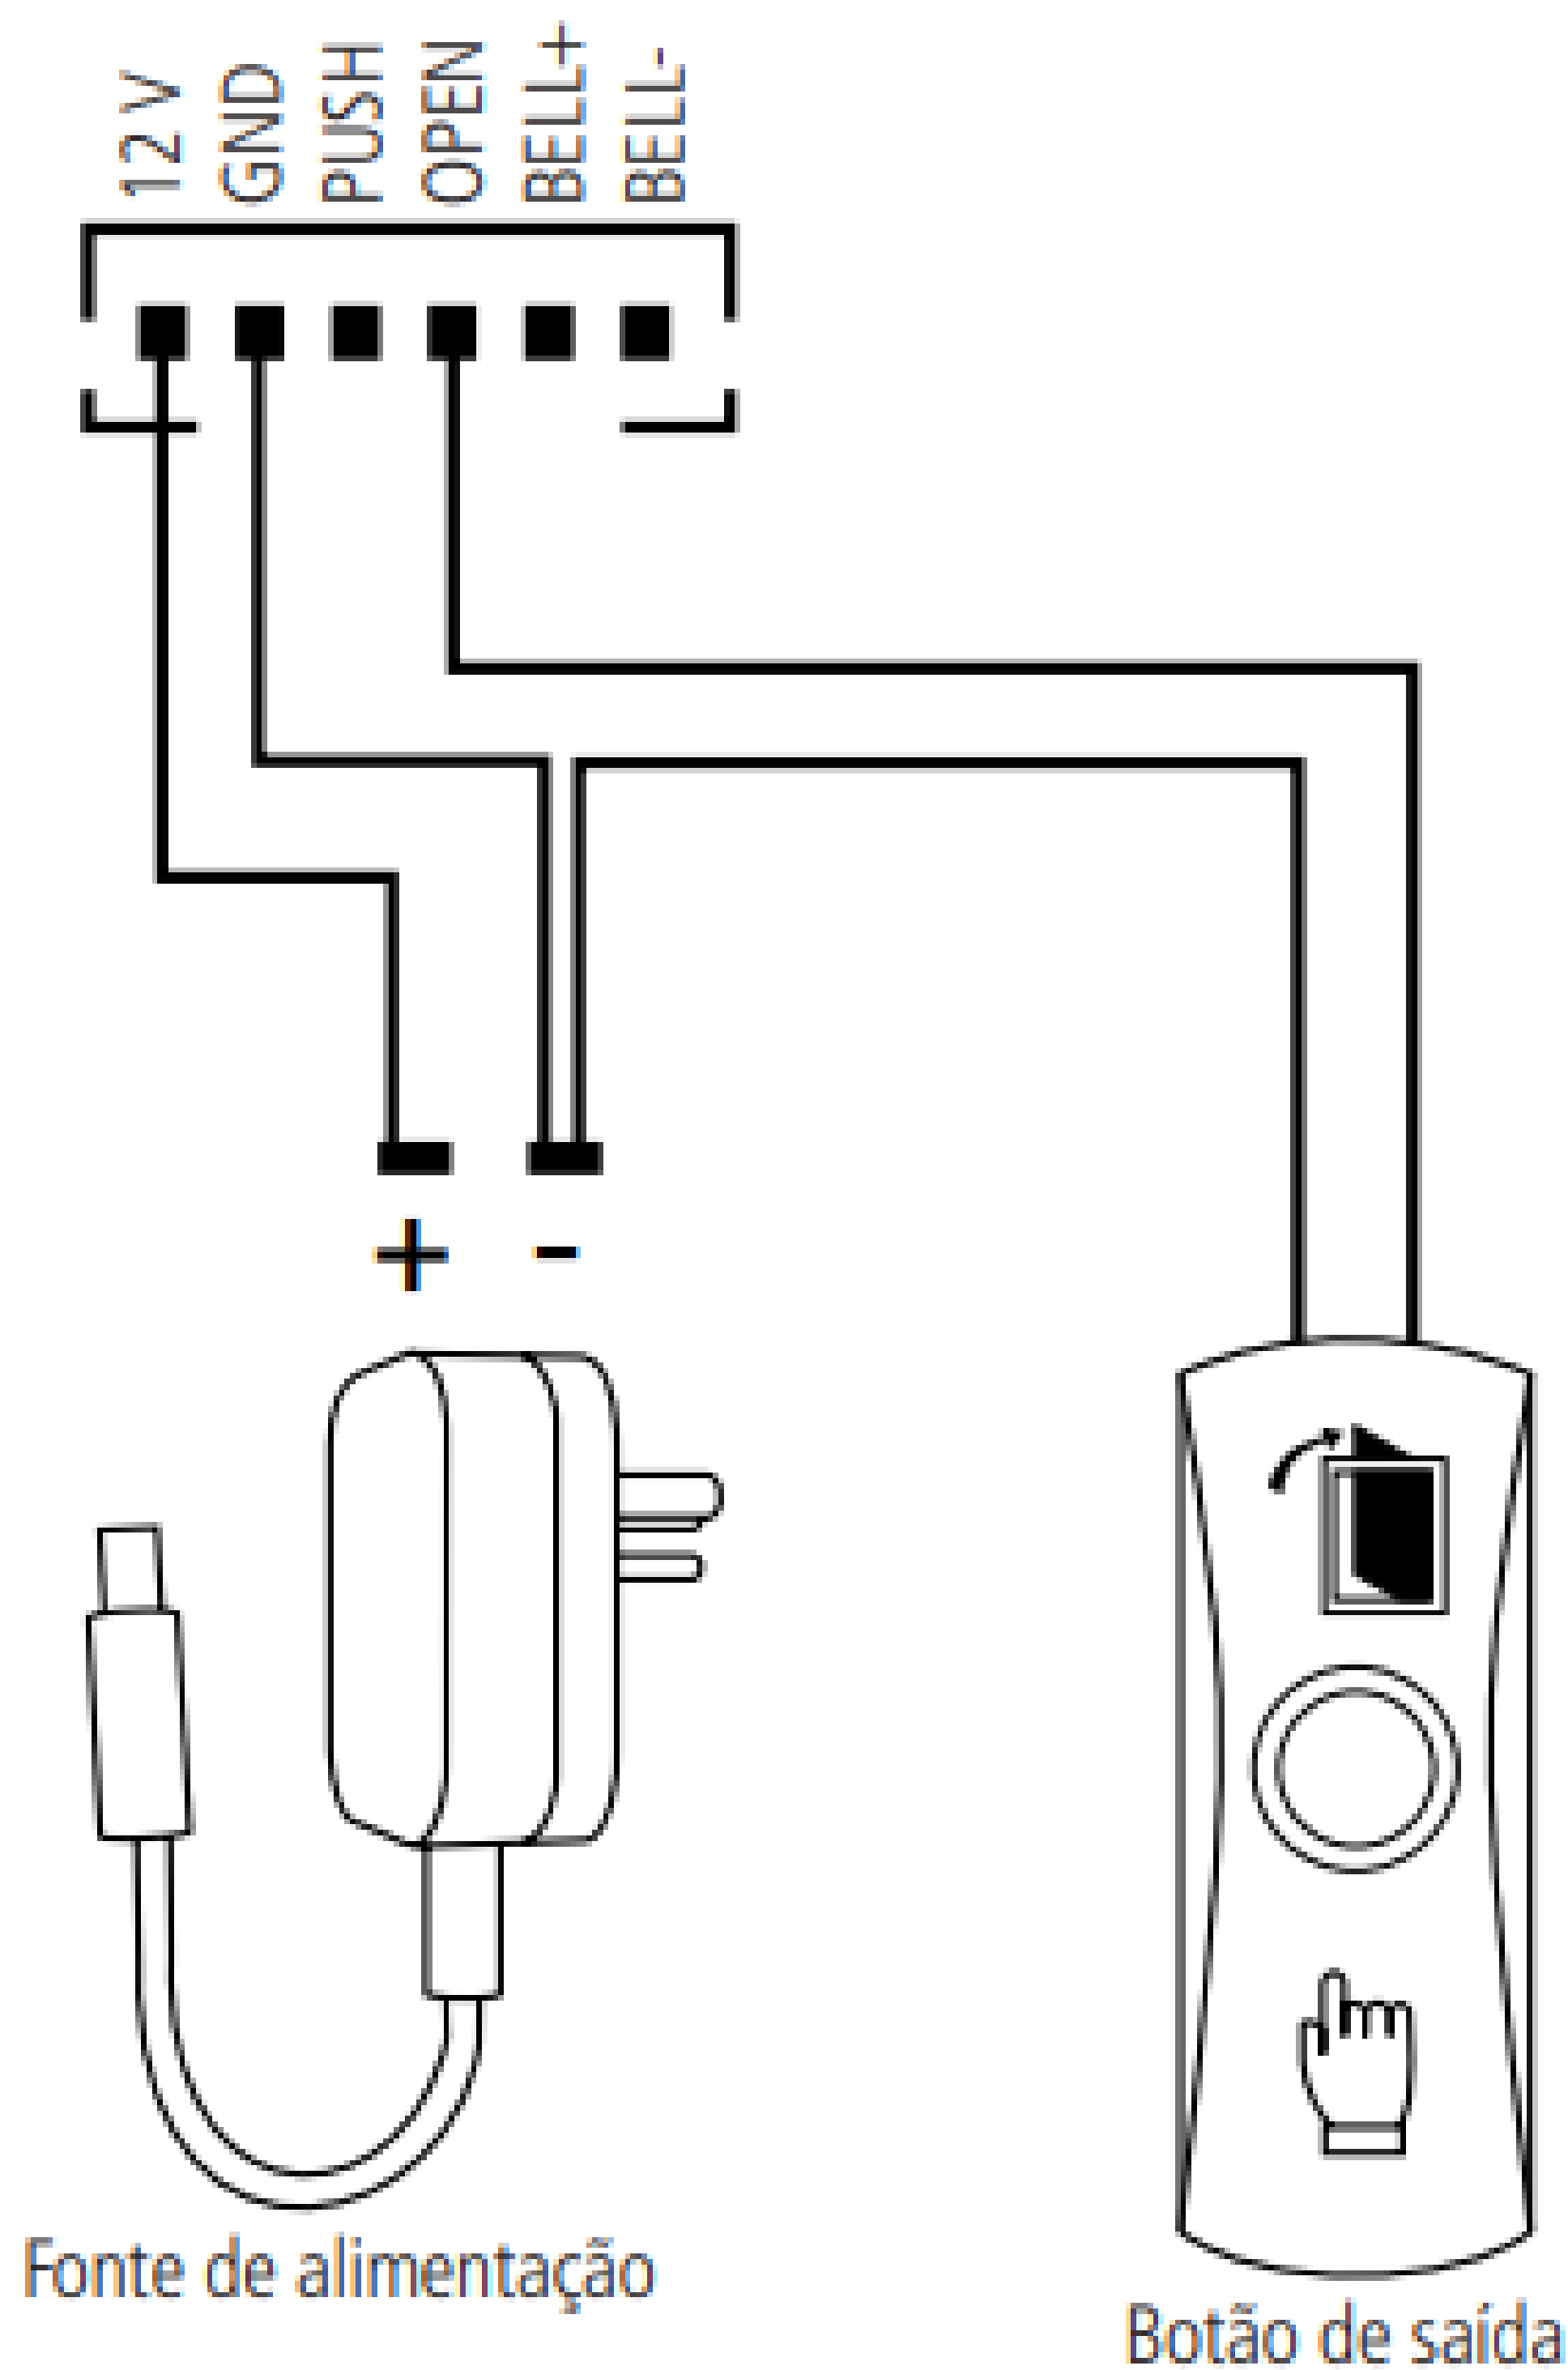


Suporte a clientes: intelbras.com/pt-br/contato/suporte-tecnico/

Vídeo tutorial: youtube.com/IntelbrasBR

(48) 2106 0006 | Segunda a sexta: 8h às 20h | Sábado: 8h às 18h

07 CAMPAINHA

A corrente admitida na saída **BELL+** e **BELL-** do controlador de acesso é **100 mA**.

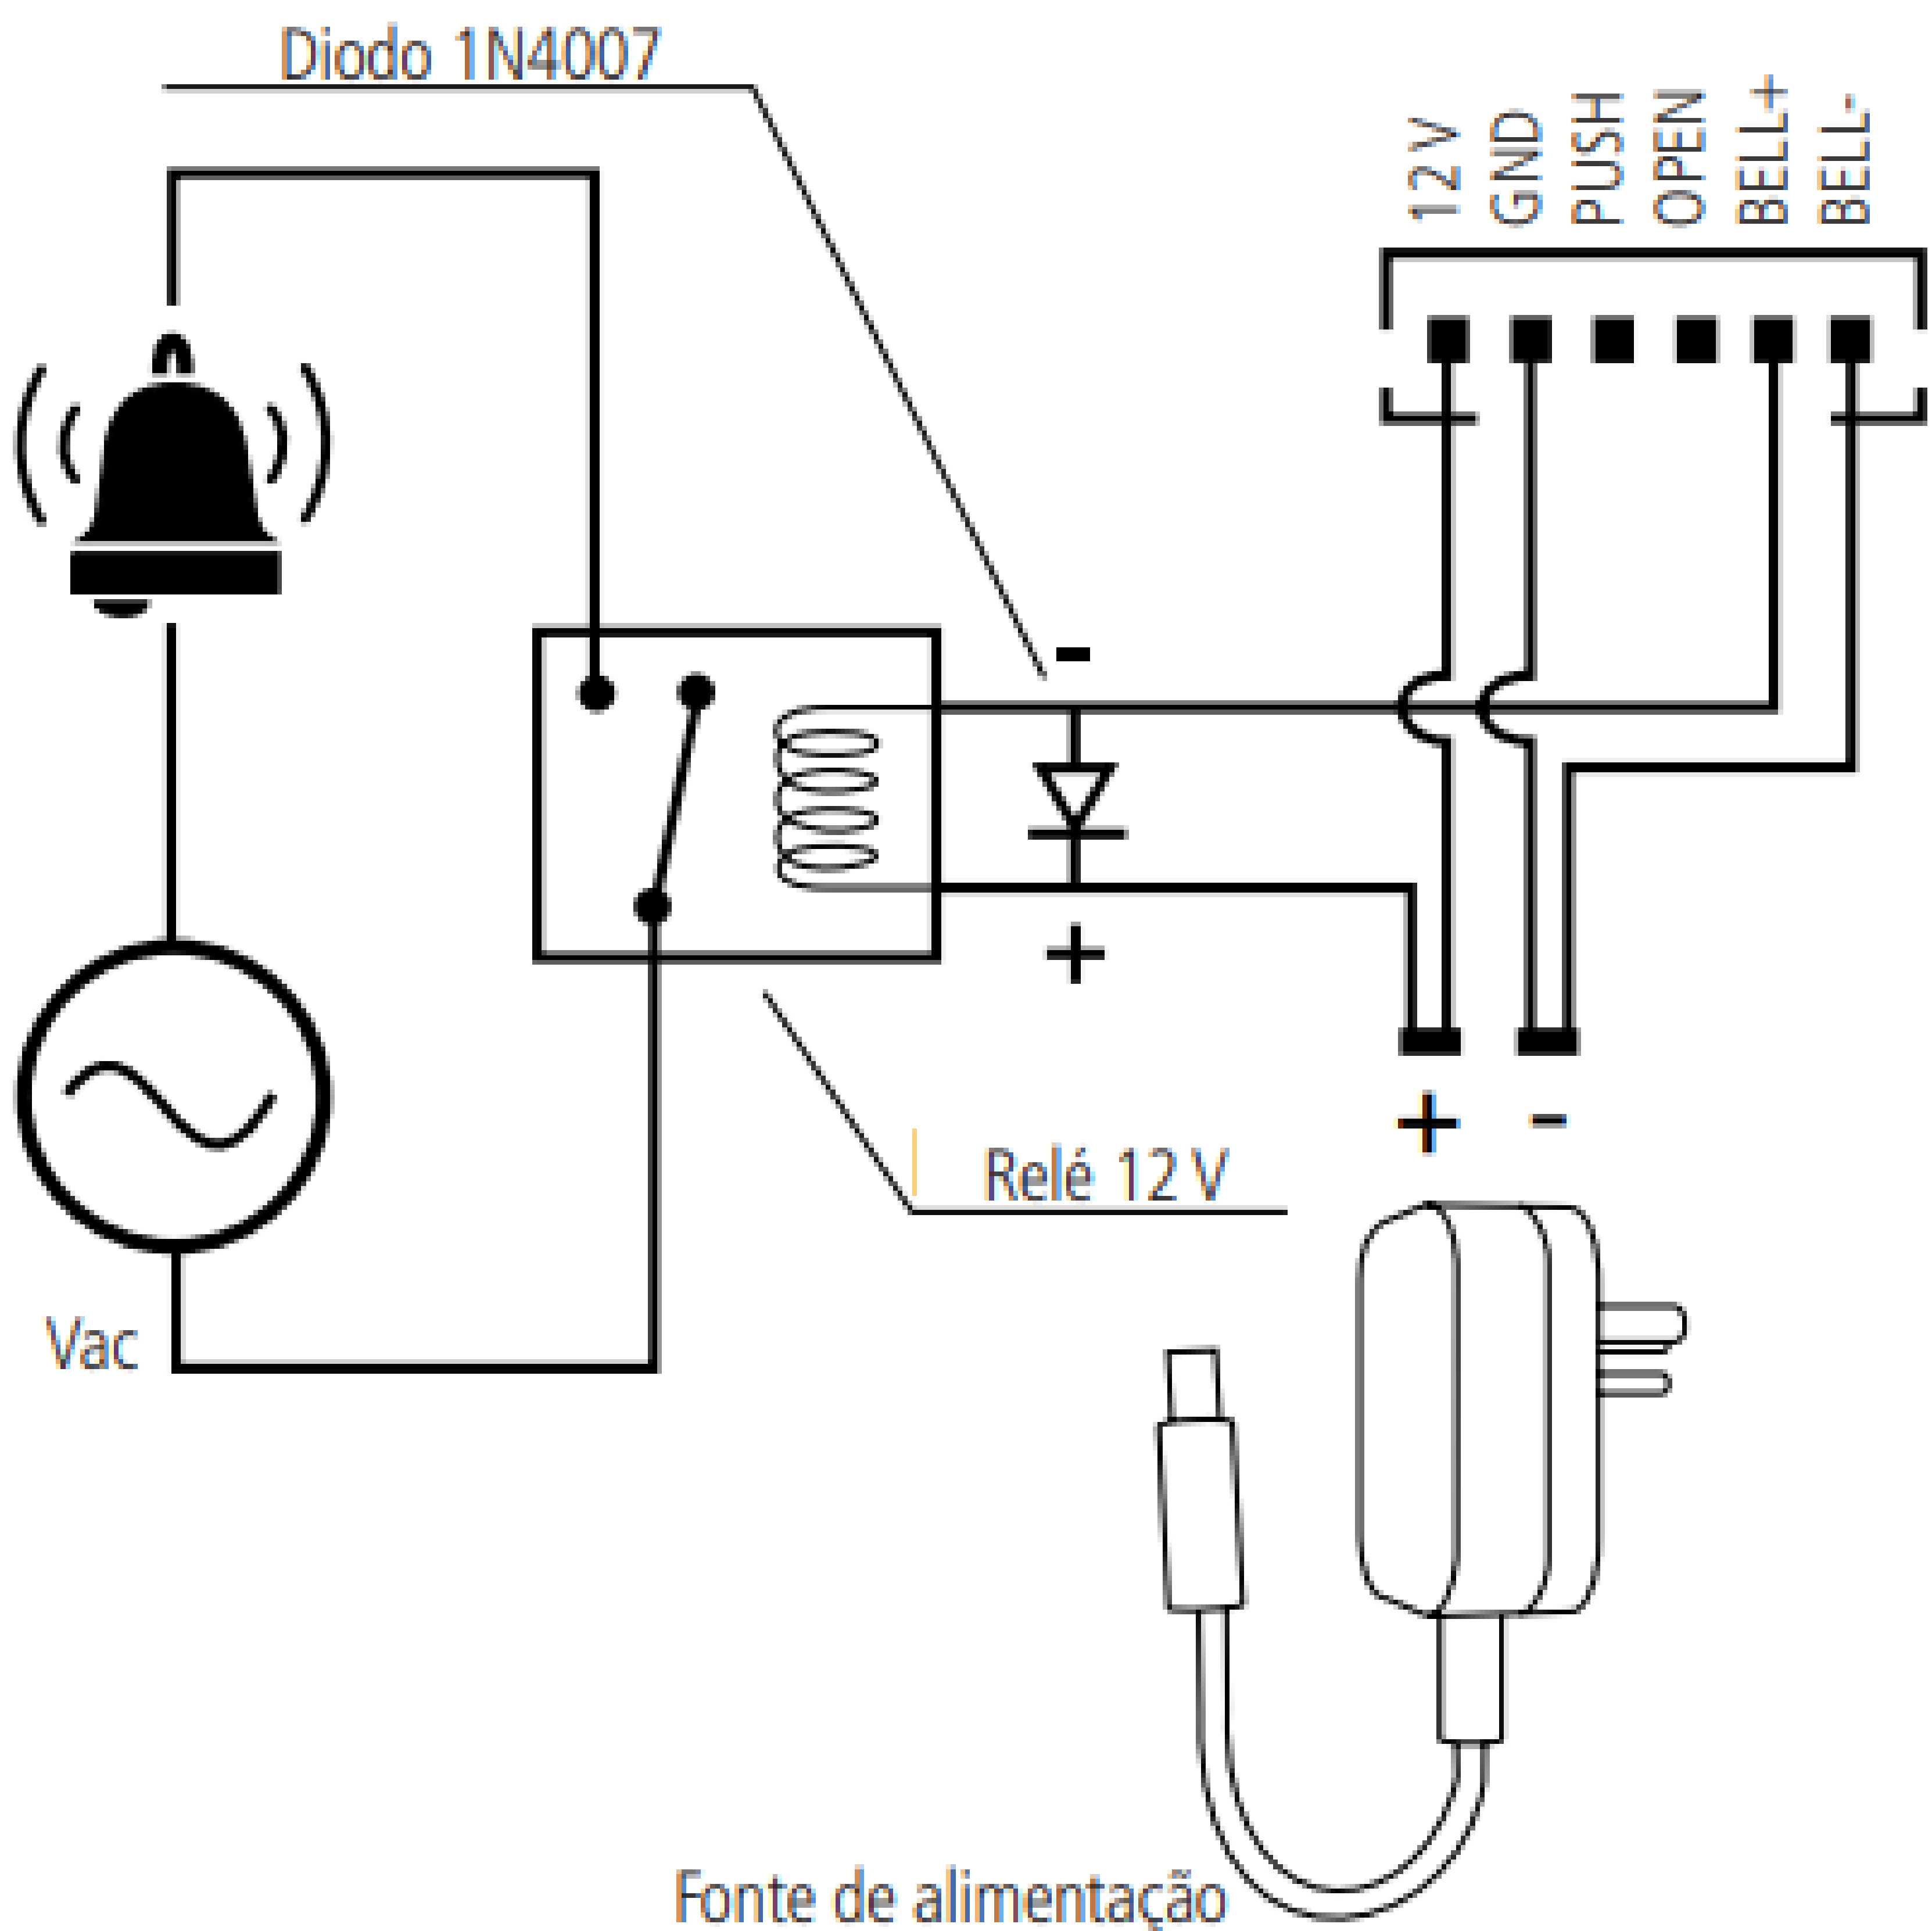

TUTORIAL TÉCNICO

Principais esquemas de ligação no controlador de acesso Digiprox SA 202

Agora você já sabe quais são os principais esquemas de ligação no controlador de acesso Digiprox SA 202. Conheça as nossas mídias clicando nos ícones abaixo!



Suporte a clientes: [intelbras.com/pt-br/contato/suporte-tecnico/](https://www.intelbras.com/pt-br/contato/suporte-tecnico/)

Vídeo tutorial: [youtube.com/IntelbrasBR](https://www.youtube.com/IntelbrasBR)

(48) 2106 0006 | Segunda a sexta: 8h às 20h | Sábado: 8h às 18h



intelbras

intelbras.com/pt-br/contato/suporte-tecnico/